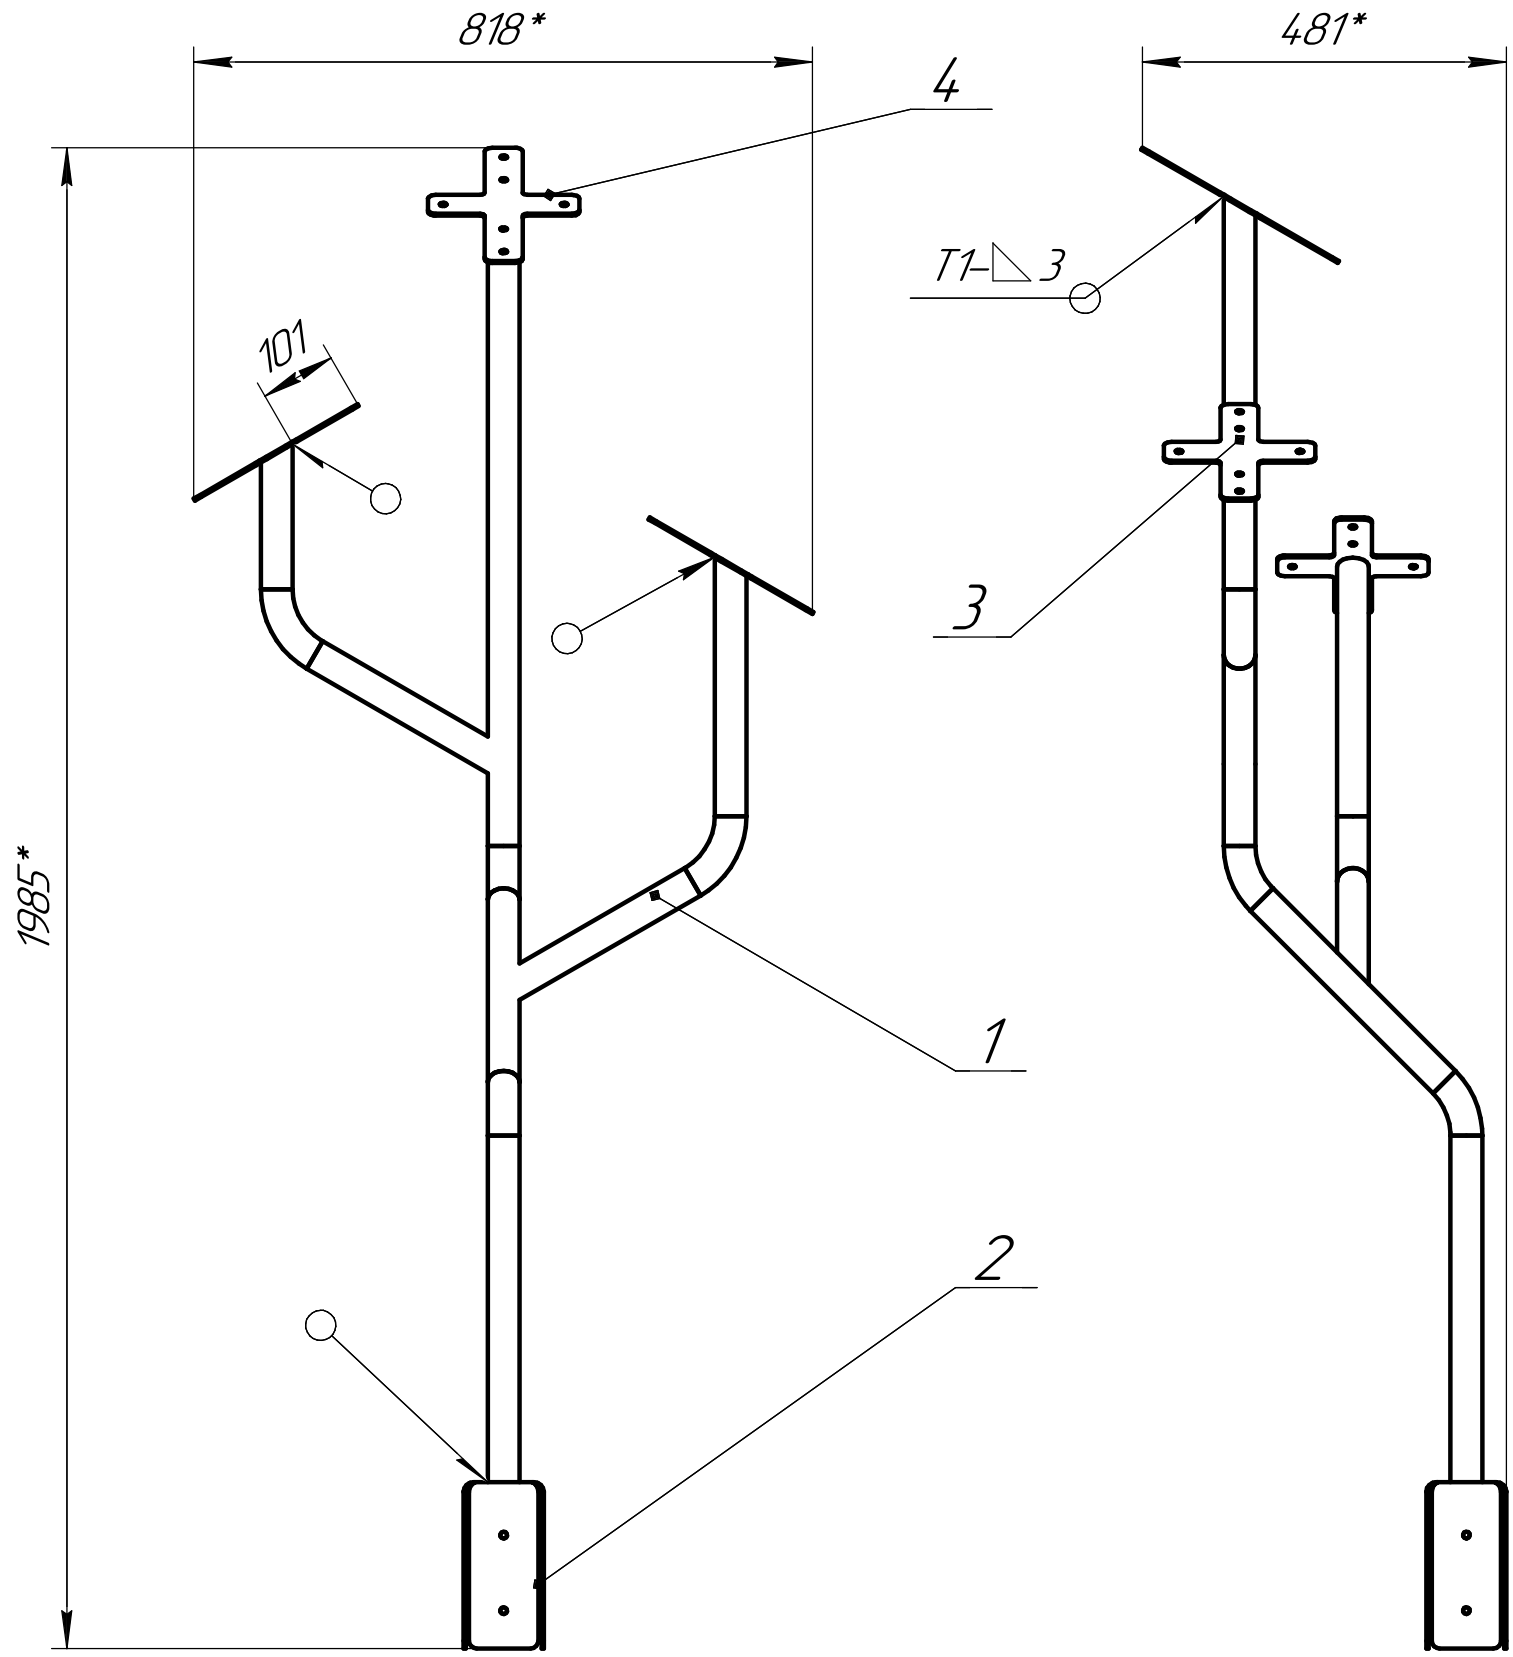

ПСР-1.29.09.100 СБ

Перв. примен.

Справ. №

Подп. и дата

Инв. № дубл.

Взам. инв. №

Подп. и дата

Инв. № подл.

1 Сварные швы по ГОСТ 14.771-76.

2 Сварочная проволока Св-08Г2С ГОСТ 2246-70.

3 * Размеры для справок.

4 Допускается обрезка, погонка по месту.

5 Покрытие порошковое полимерное. Цвет согласно цветовому паспорту.

Изм.	Лист	№ докум.	Подп.	Дата	ПСР-1.29.09.100 СБ		
Разраб.		Минченков А.М.			Ветки Сборочный чертеж	Лит.	Масса 24,61 / Масштаб 1:10
Пров.		Гладков В.В.				Лист	Листов 1
Т.контр.		Гладков В.В.				ООО "Производственная компания "Модуль"	
Н.контр.							
Утв.		Родионов С.В.					

Копировал

Формат А3