



1 шт ЭС

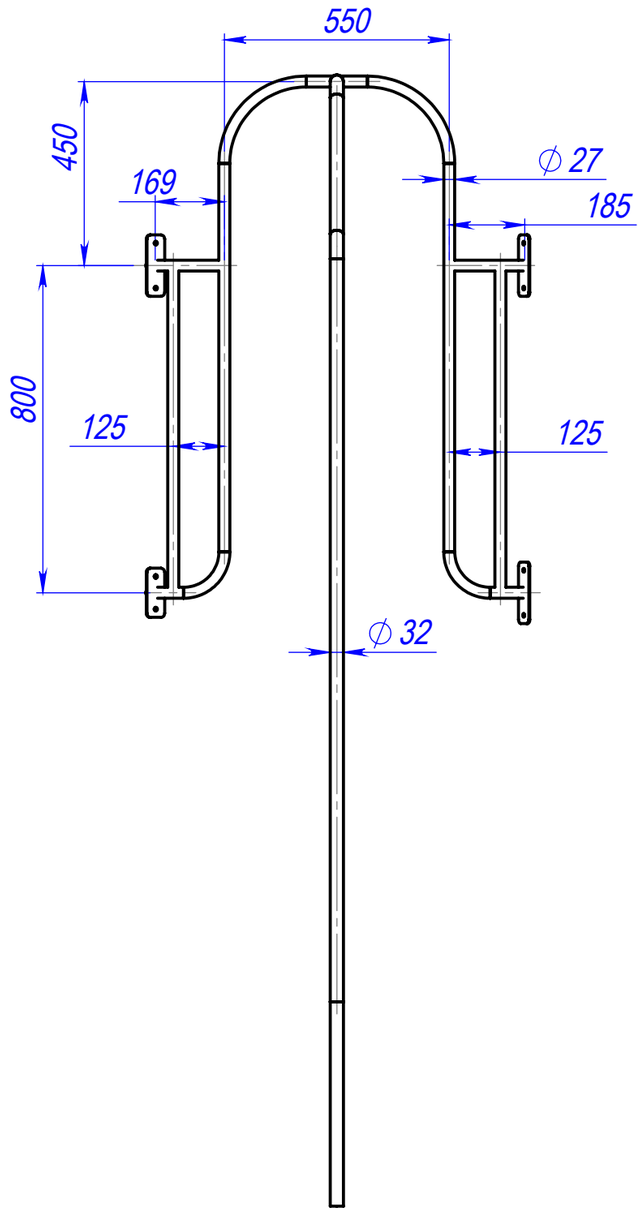


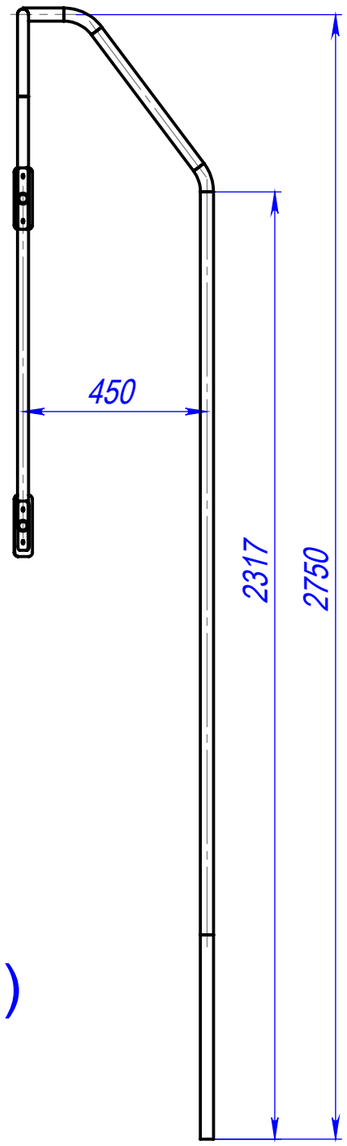

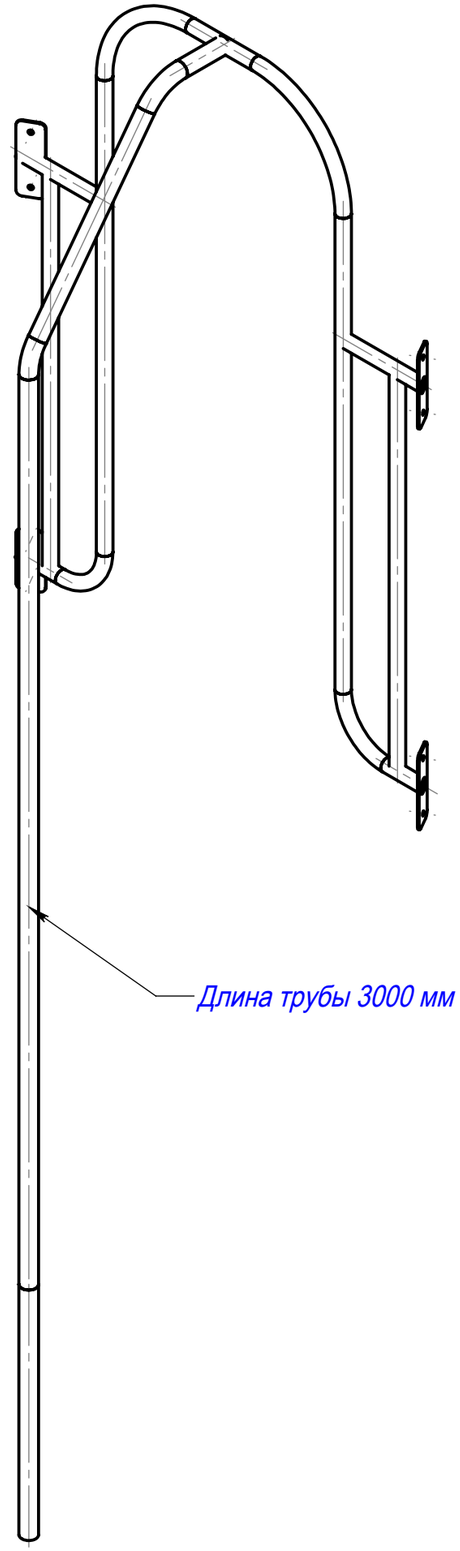


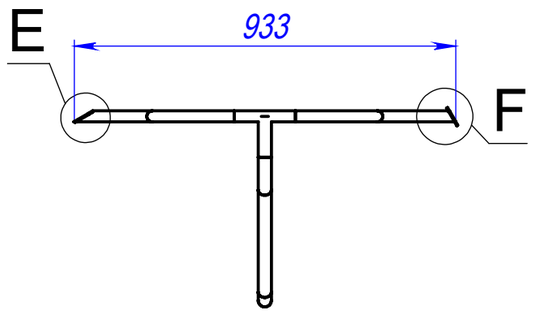

E (1 : 3)

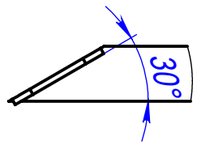

F (1 : 3)

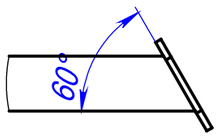

Изм.	Лист	№ докум.	Подп.	Дата	*Пожарный спуск с аркой*	Лист 6

Подп. и дата | Инв. № дубл. | Взам. инв. № | Подп. и дата | Инв. № подл.