


ШЭ630

МЕСТНЫЙ А
МАСШТАБ 2 : 15

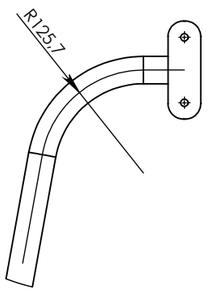


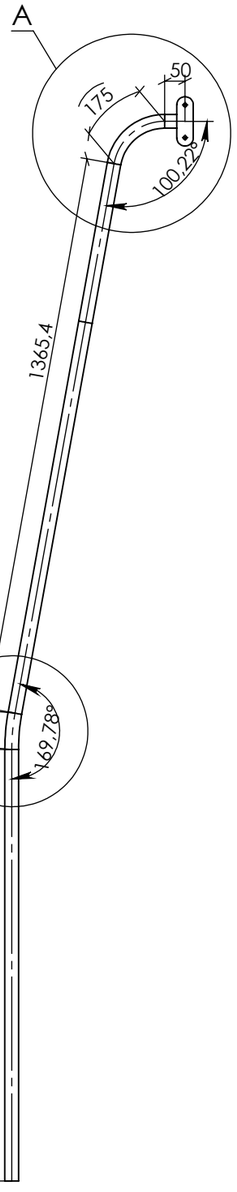



МЕСТНЫЙ В
МАСШТАБ 2 : 15

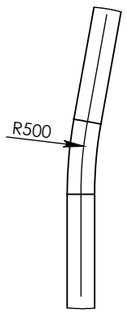


СЕЧЕНИЕ С-С
МАСШТАБ 1 : 15

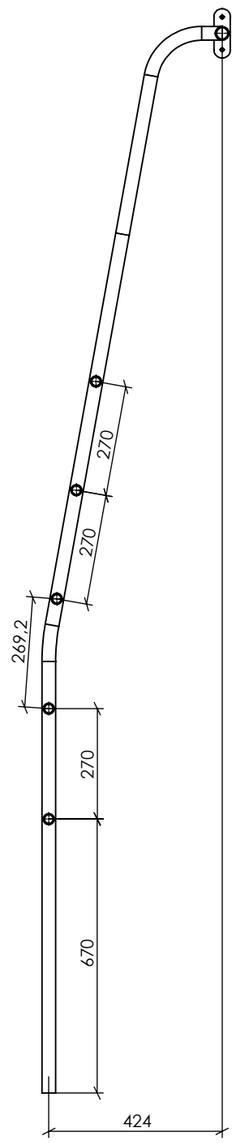

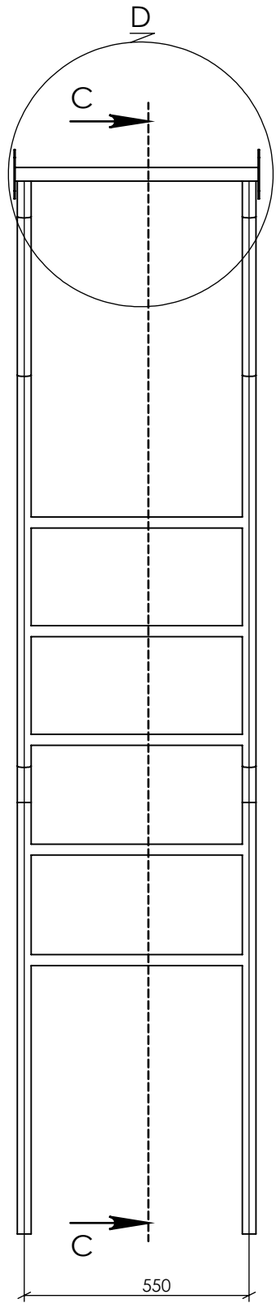

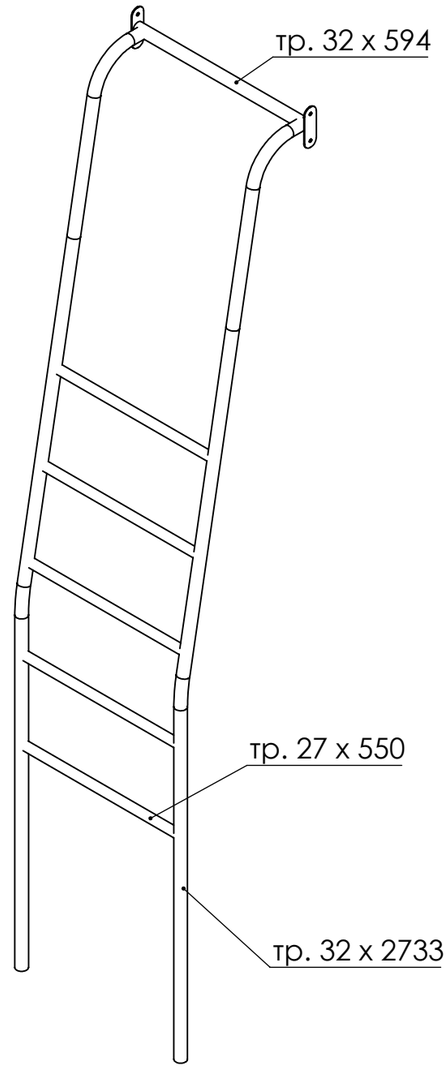

МЕСТНЫЙ D
МАСШТАБ 2 : 15

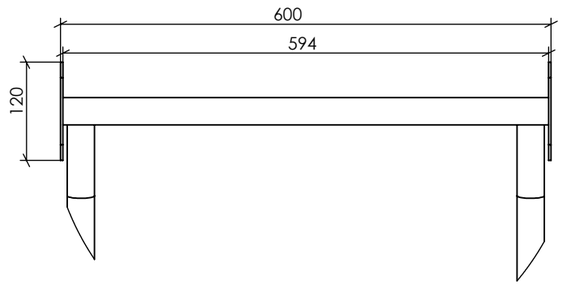

Изм.	Лист	№ докум.	Подп.	Дата	Лесенка приставная гнутая 2400	Лист 1

Подп. и дата | Инв. № дубл. | Взам. инв. № | Подп. и дата | Инв. № подл.

А

Файл: Лестница большая икстр-5.04