
СБ

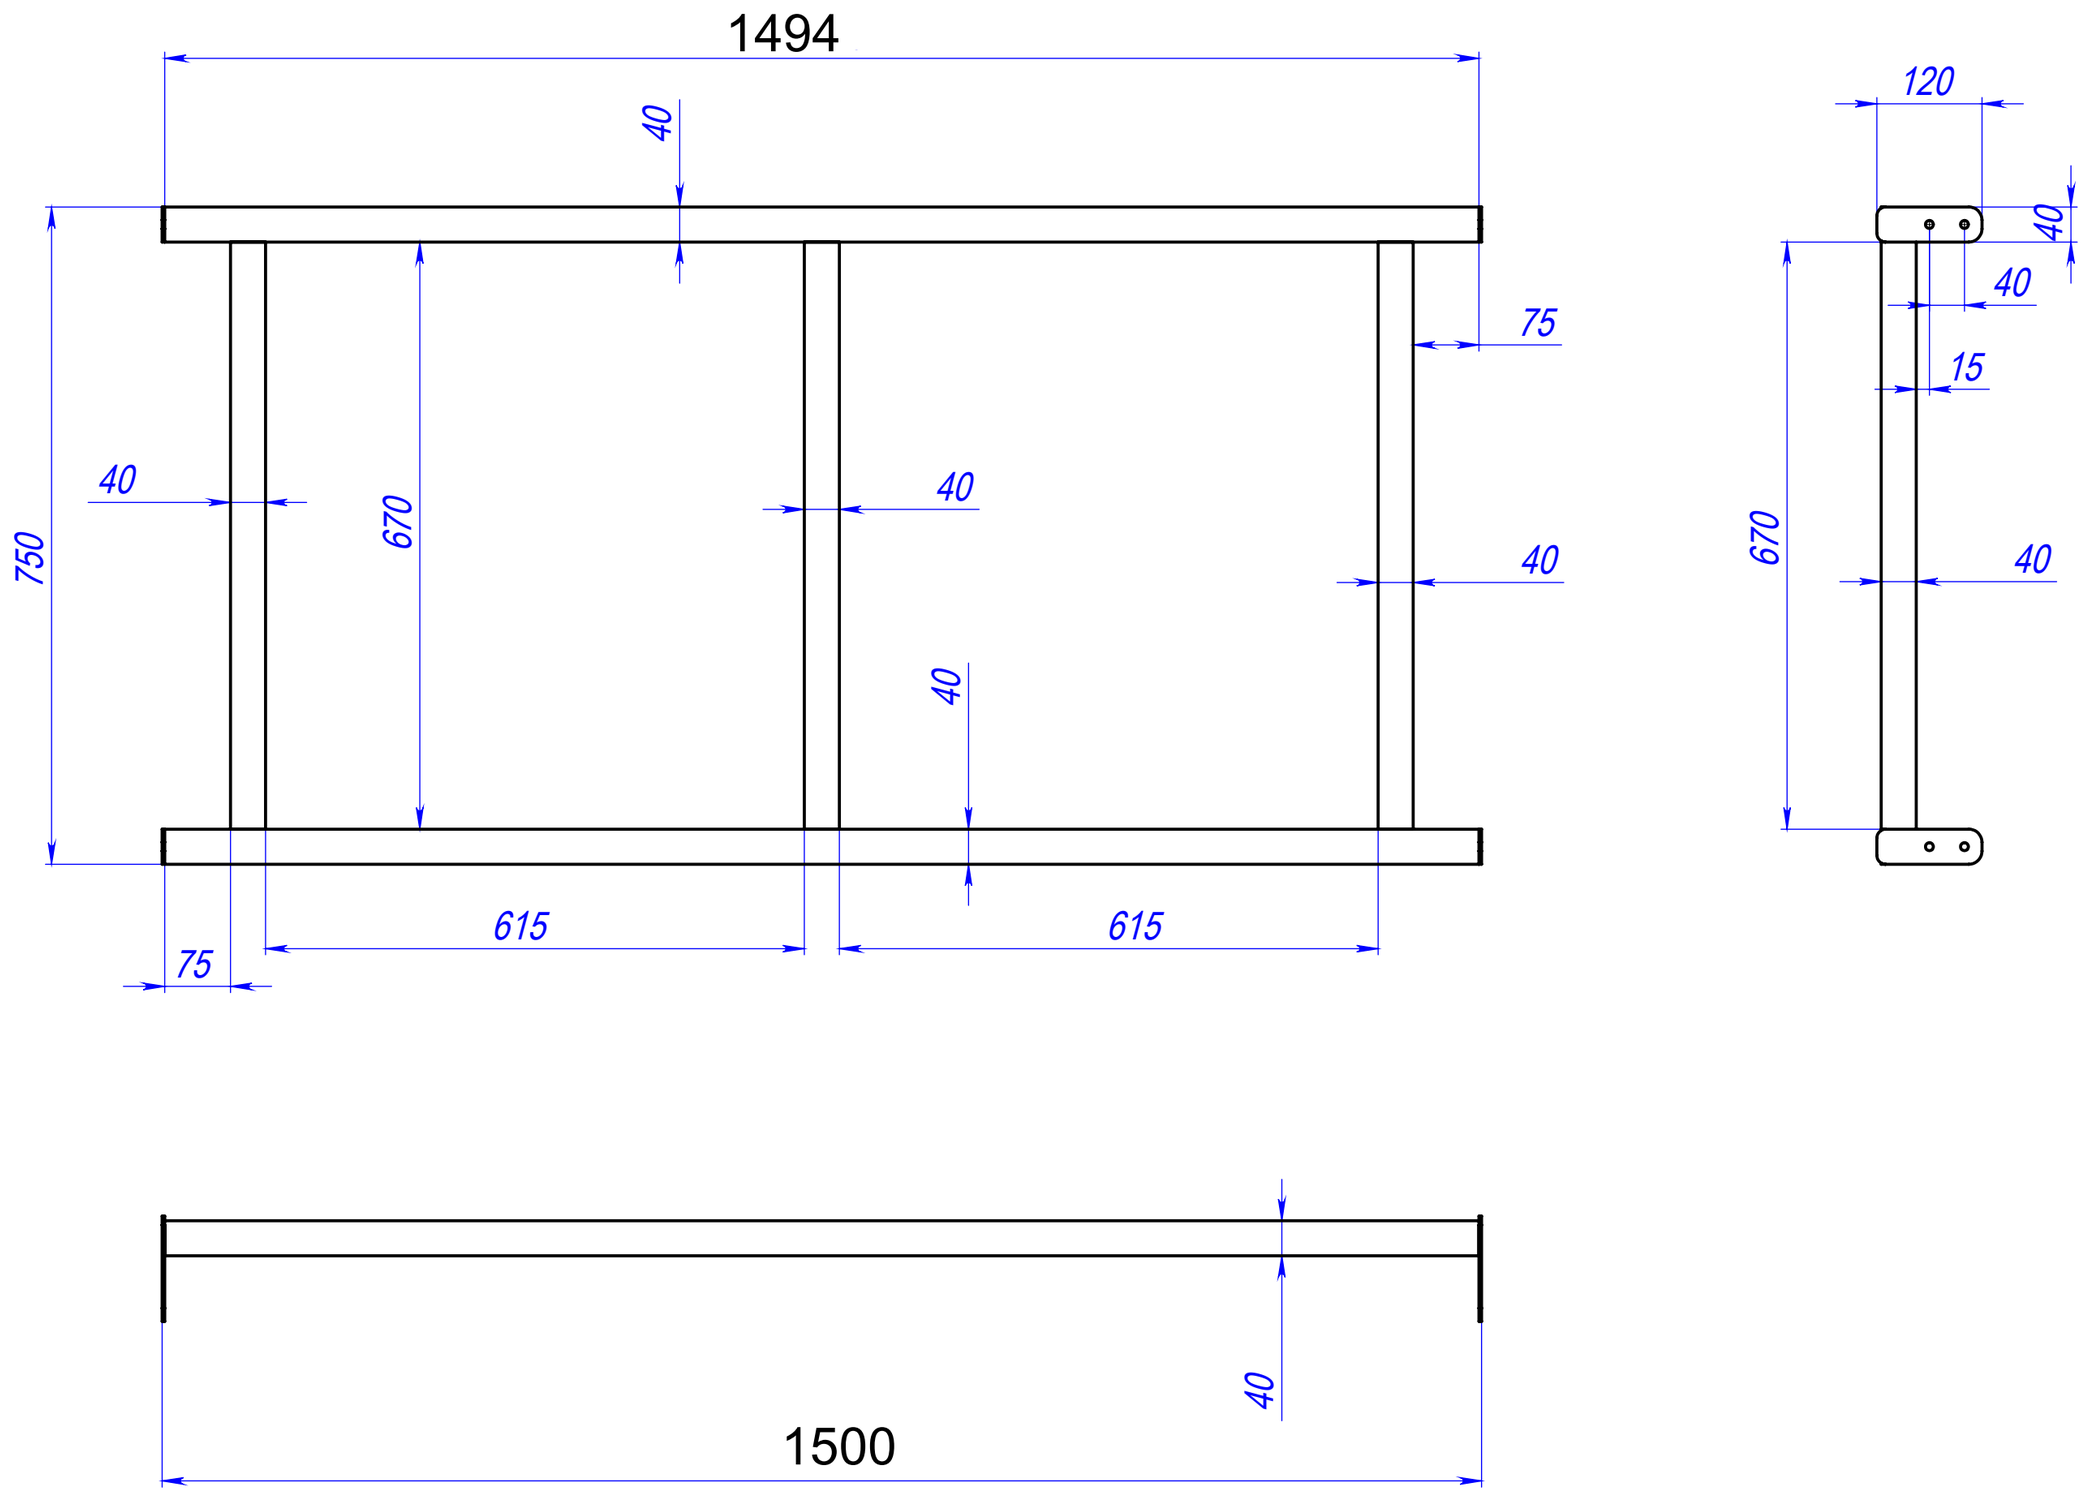

Изм.	Лист	№ докум.	Подп.	Дата	Каркас моста металлического прямого 1500х750	Лист 3

Подп. и дата | Инв. № дубл. | Взам. инв. № | Подп. и дата | Инв. № подл.