


Каркас моста наклонного
2000мм

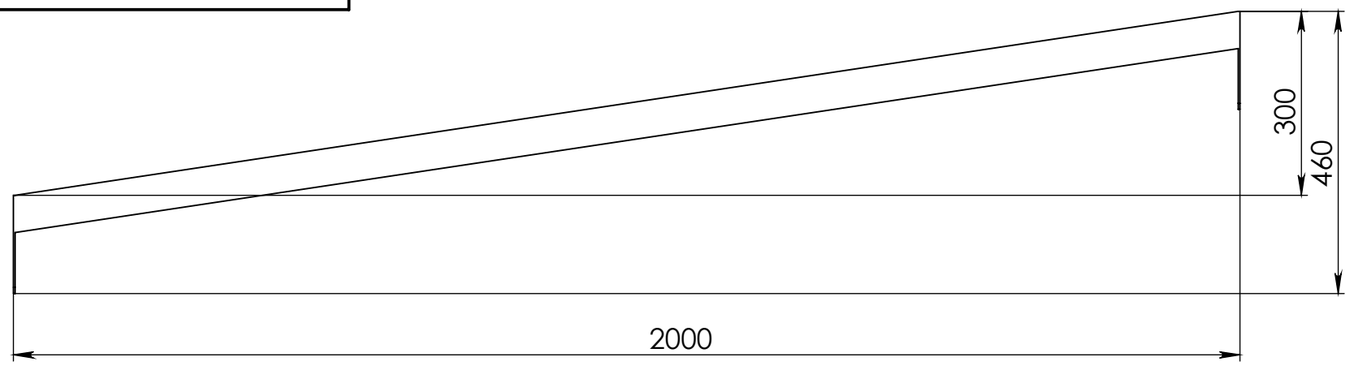


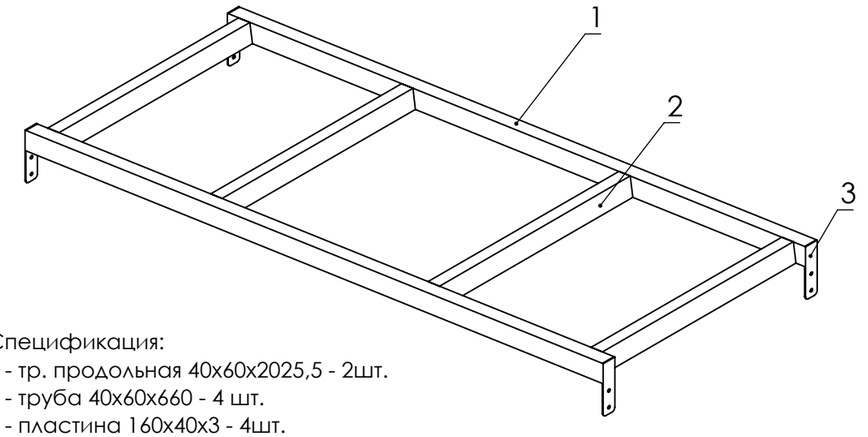


Спецификация:
1 - тр. продольная 40х60х2025,5 - 2шт.
2 - труба 40х60х660 - 4 шт.
3 - пластина 160х40х3 - 4шт.

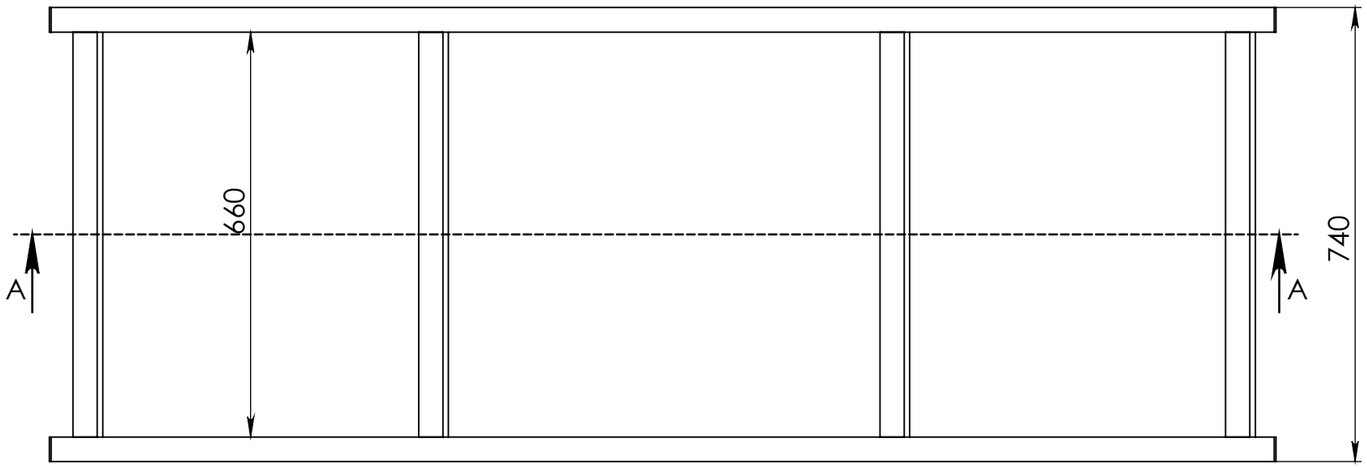


СЕЧЕНИЕ А-А
МАСШТАБ 1 : 10

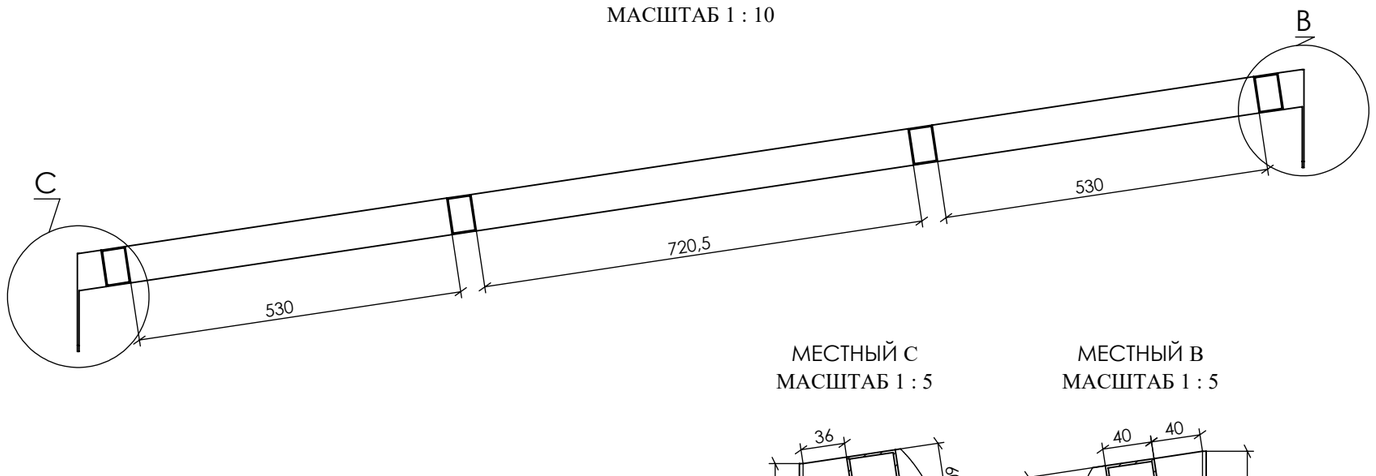


МЕСТНЫЙ С
МАСШТАБ 1 : 5

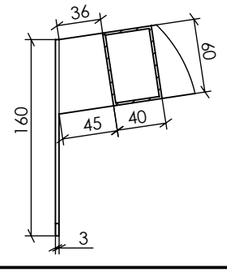


МЕСТНЫЙ В
МАСШТАБ 1 : 5

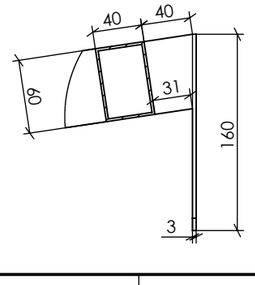

тр. продольная 40х60х2025

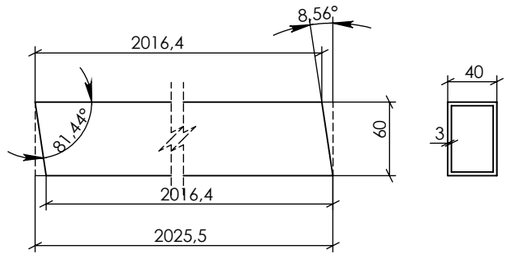

пластина 160х40х3

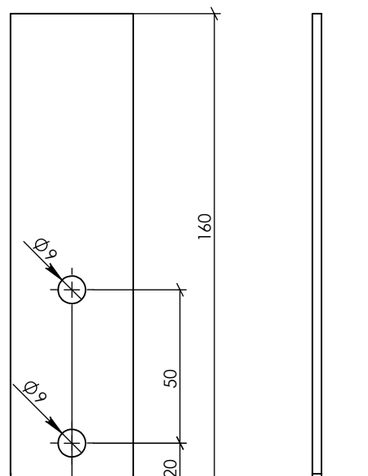

Изм.	Лист	№ докум.	Подп.	Дата	Каркас моста наклонного 2000мм	Лист 1

Подп. и дата | Инв. № дубл. | Взам. инв. № | Подп. и дата | Инв. № подл.

Файл: Каркас моста наклонного 2000х750мм h=300