



СБ

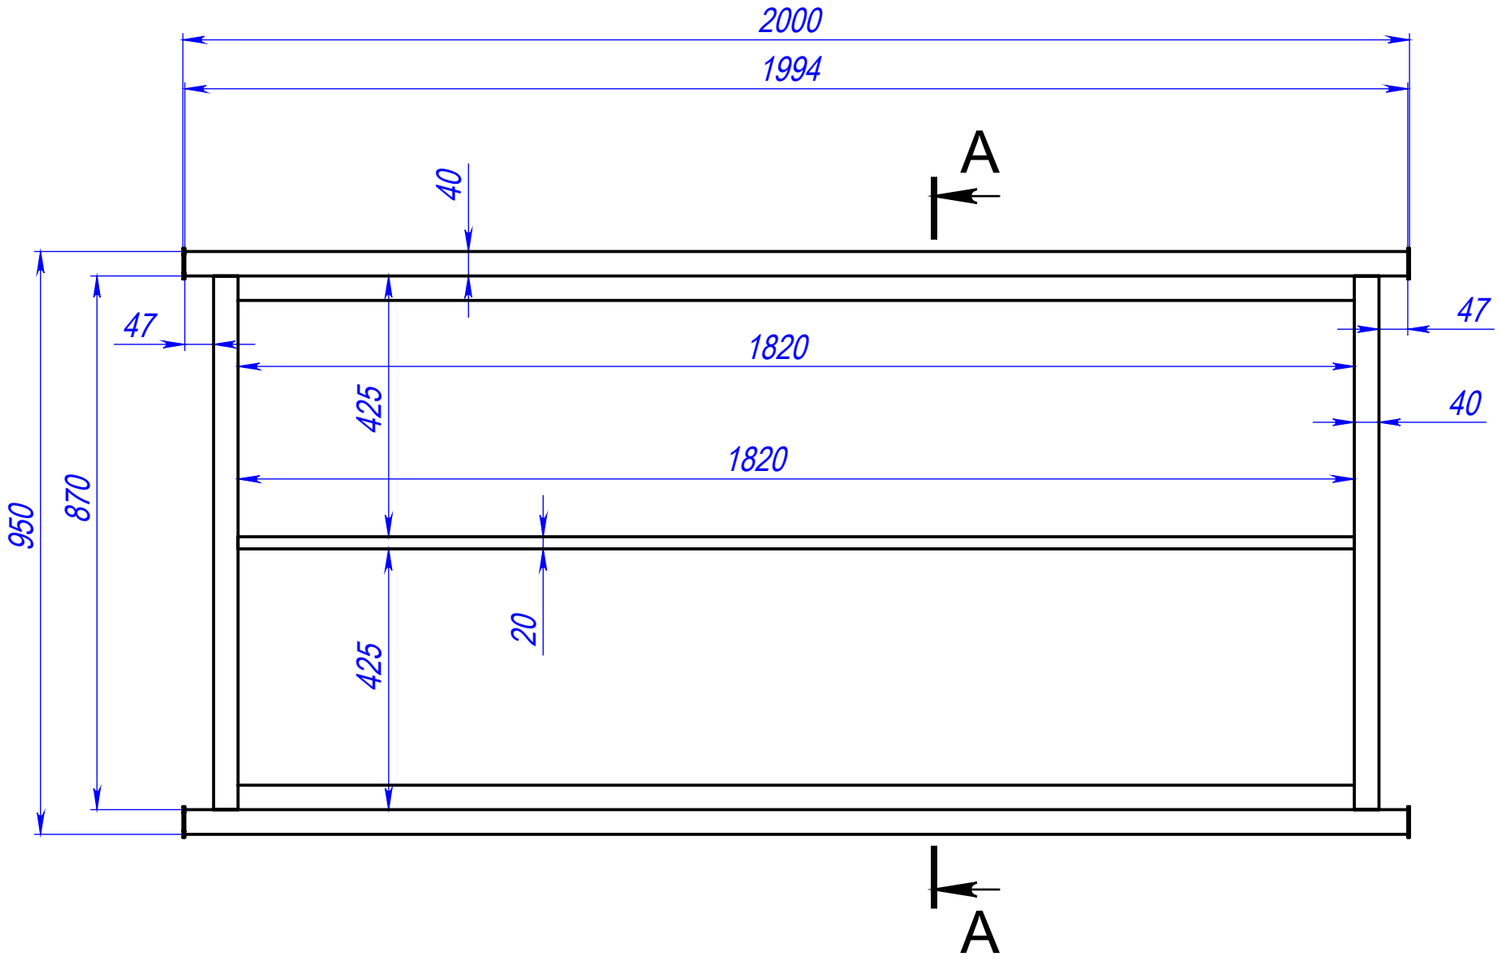

A-A (1 : 10)

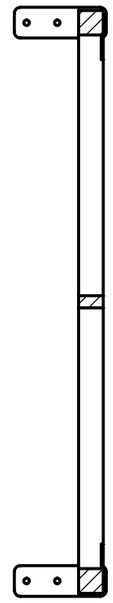

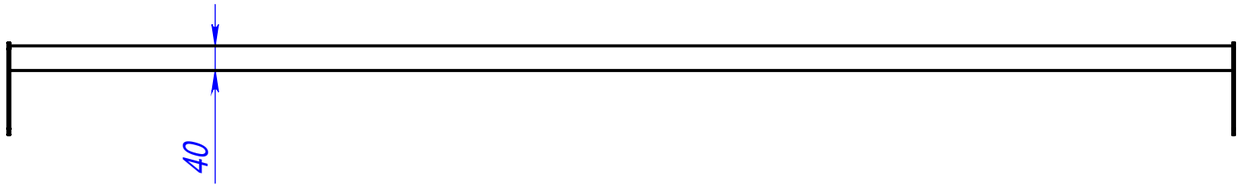

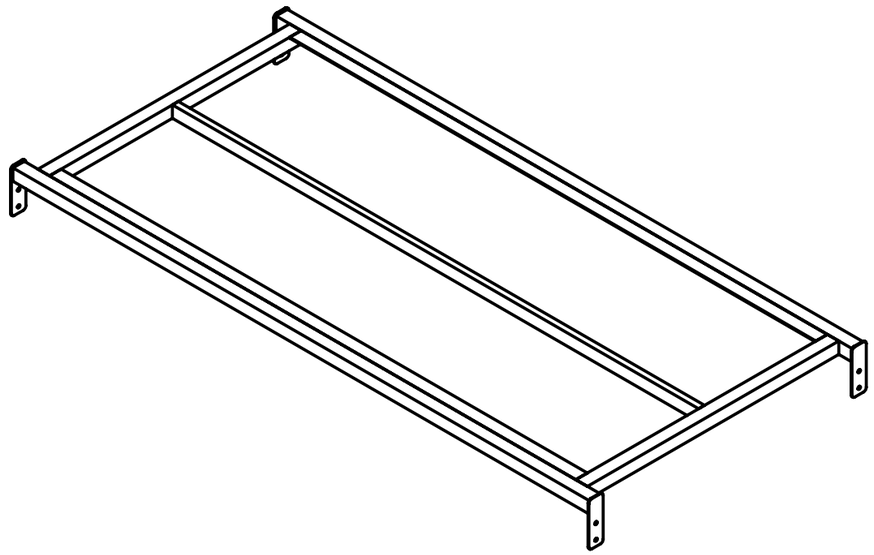

Изм.	Лист	№ докум.	Подп.	Дата	Мостик прямой 2000х950 мм	Лист 7

Подп. и дата | Инв. № дубл. | Взам. инв. № | Подп. и дата | Инв. № подл.