



СБ

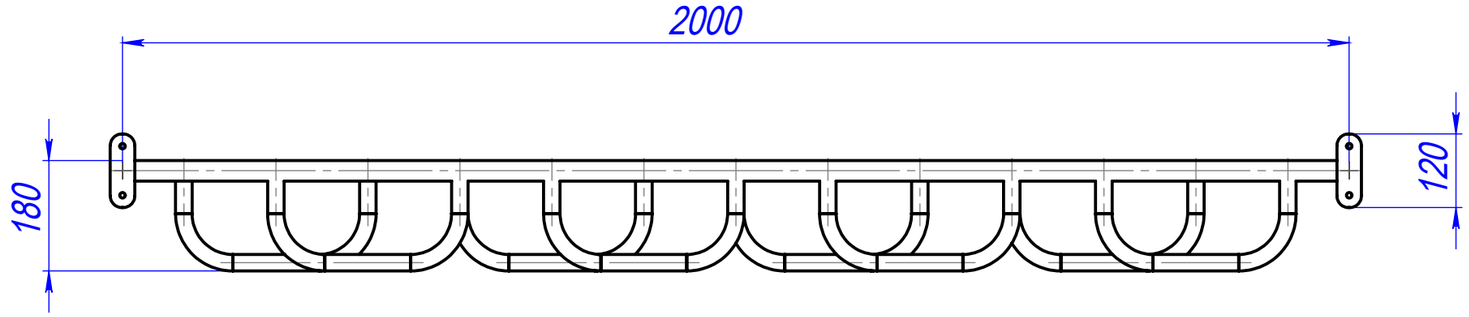


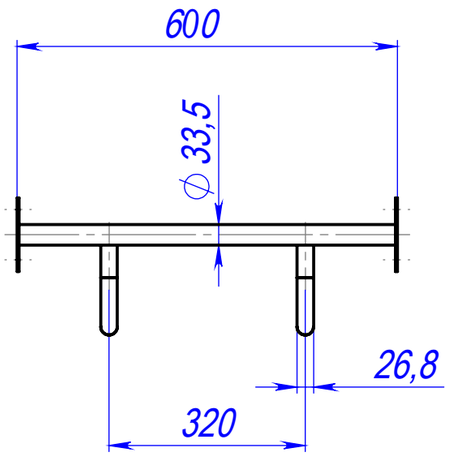

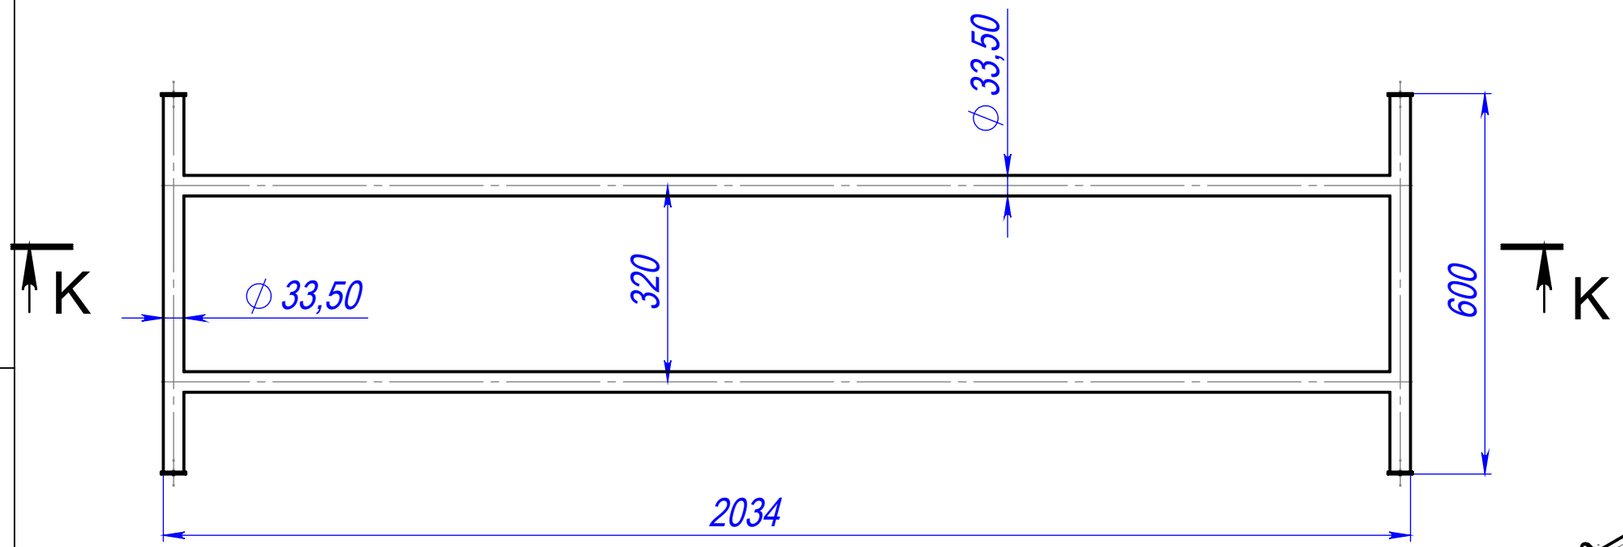

K-K (1 : 10)

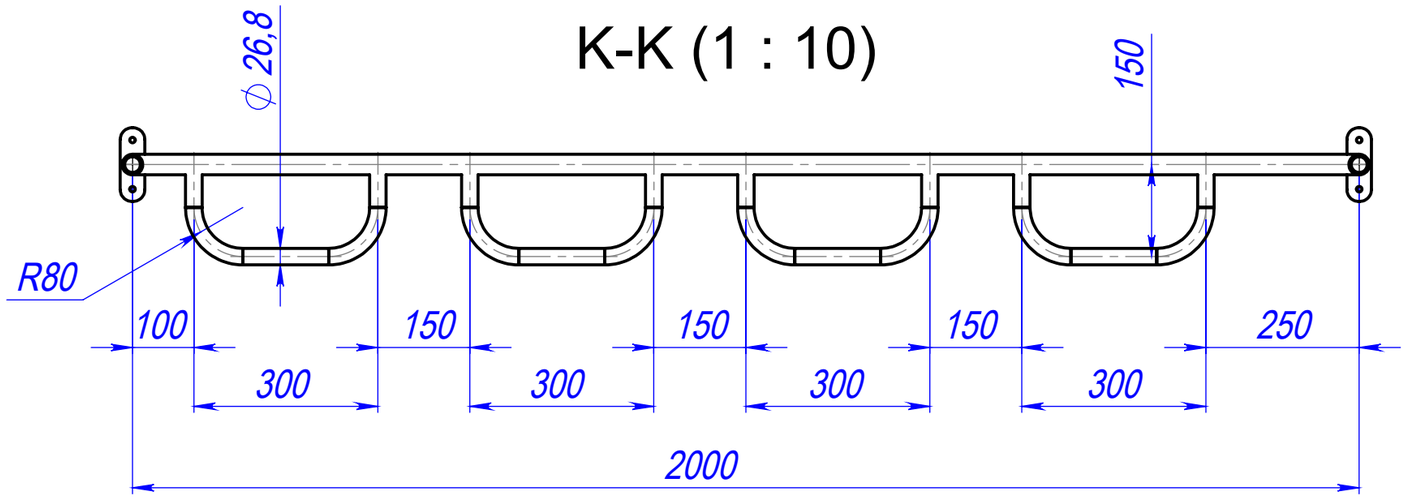

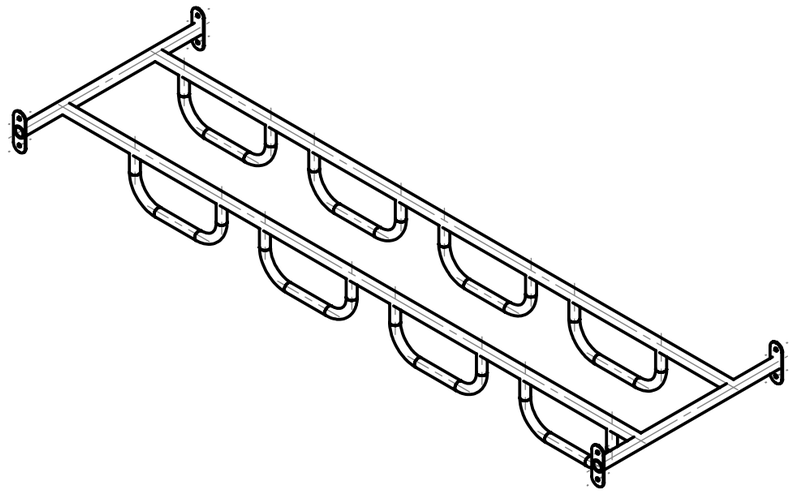

Изм.	Лист	№ докум.	Подп.	Дата	Рукоход перекидной	Лист 1

Подп. и дата | Инв. № дубл. | Взам. инв. № | Подп. и дата | Инв. № подл.