



МЕСТНЫЙ А
МАСШТАБ 1 : 6

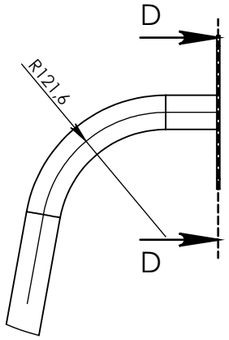


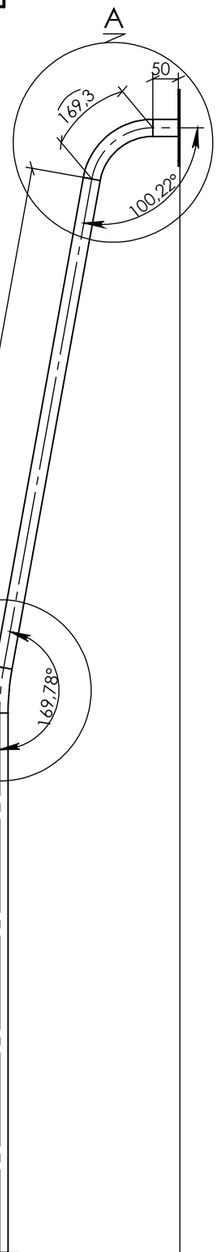


СЕЧЕНИЕ С-С
МАСШТАБ 1 : 12

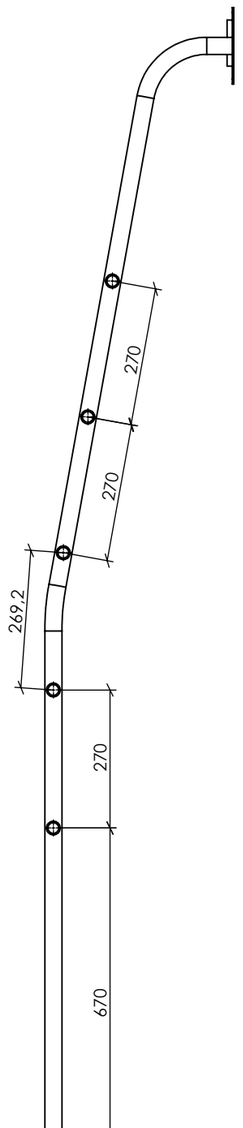

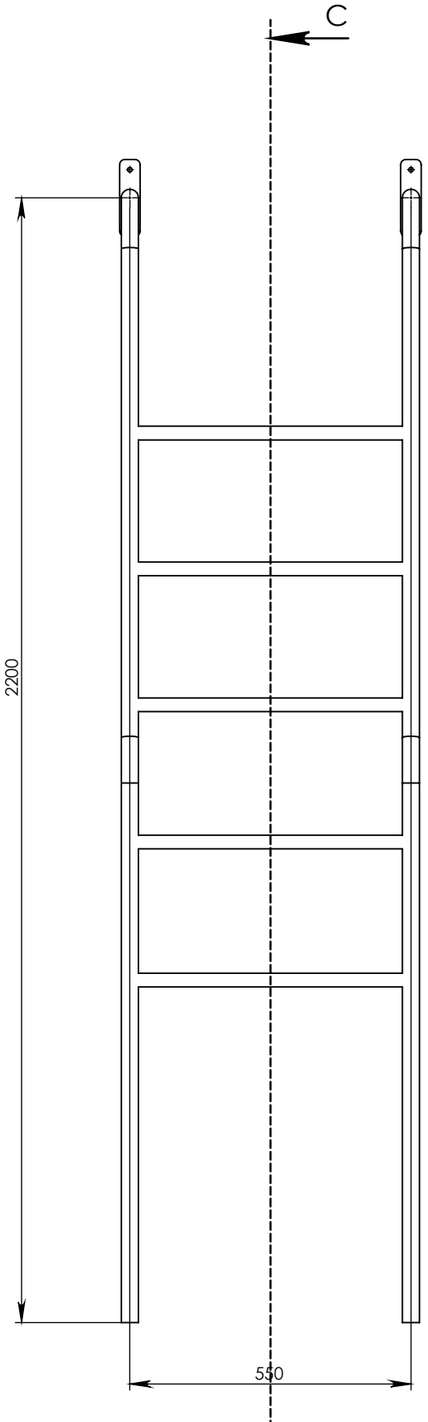

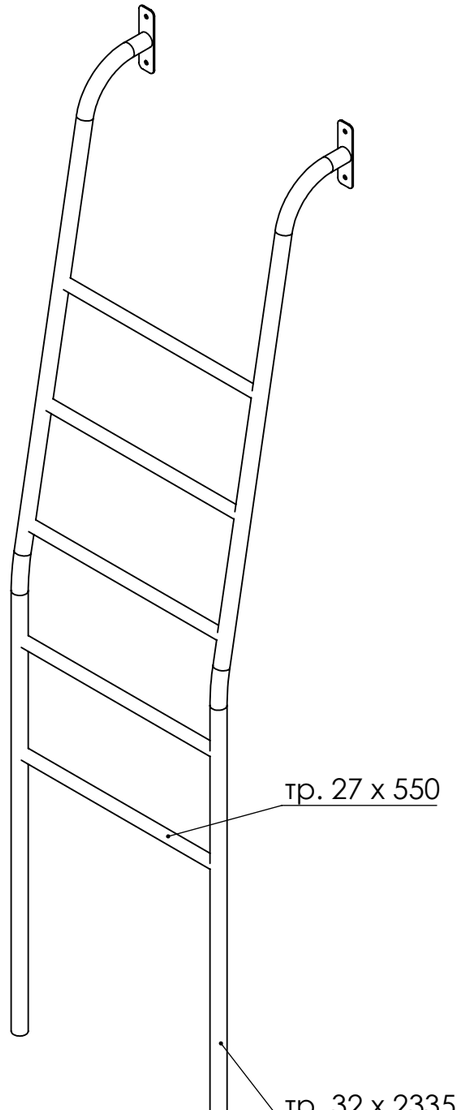

МЕСТНЫЙ В
МАСШТАБ 1 : 6

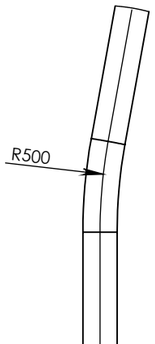

СЕЧЕНИЕ D-D
МАСШТАБ 1 : 3

Изм.	Лист	№ докум.	Подп.	Дата	Лесенка приставная гнутая 1800	Лист 1

Подп. и дата | Инв. № дубл. | Взам. инв. № | Подп. и дата | Инв. № подл.

Файл: Лестница малая икстр-5.04